PORTFOLIO

VIRGIL LETEURTRE
SÉLECTION DE TRAVAUX 2021-2026

Architecture d'intérieure · Design



PORTFOLIO

Architecture d'intérieure · Design

Virgil Leteurtre

LISAA Bordeaux 2025 - 2026

SOMMAIRE

01	Membrane	3-6
02	Le Règne animal	7
03	NAL	8-9
04	Obadia	10-11
05	Hegoburu	12-13
06	Dubon	14-15
07	Montgiron	16-18
08	OSE	19-20
09	Le refuge	21-22
10	Fracture	23-24

MEMBRANE

Rénovation d’une école de musique

Le CIAM occupe un ensemble bâti hétérogène, hérité d’agrandissements successifs : un bâtiment principal donnant sur la rue, d’anciennes écuries et une cour intérieure reliant les différentes parties de l’école. Les circulations sont étroites, les niveaux s’enchaînent difficilement et les flux manquent de lisibilité.

La pratique musicale sature constamment l’espace. Le bruit est nécessaire à l’apprentissage, mais rien dans le bâtiment n’offre de véritable temps de recul : les salles se touchent, le couloir n’est qu’un passage et l’oreille ne se repose jamais.

Le projet ne cherche pas à supprimer cette intensité. Il lui donne une respiration, en transformant la circulation elle-même en espace de repos, de rencontre et de transition acoustique.

Contexte	Projet de fin d’études — LISAA Bordeaux
Année	2025 — 2026
Programme	Rénovation d’une école de musique et de sa salle de concert
Rôle personnel	Projet mené seul
Focus présenté	Concept, circulation, mobilier acoustique
Documents	Plans, coupe, images de synthèse, essai acoustique

VALEURS AJOUTÉES

01 Transformer la circulation en espace habité

02 Faire du couloir une membrane acoustique et sociale

03 Créer un mobilier continu, modulable et absorbant

04 Relier salles de cours, jam, concert et cour intérieure



Façade sur rue — la projection des dates de concert rend l’activité de l’école visible depuis la ville.



La cour intérieure et l’extension bois reliant le bâtiment principal aux anciennes écuries.

LE CONCEPT

Une membrane habitée : le couloir cesse d'être un passage pour devenir l'organe qui sépare, filtre et régule les intensités de l'école.

Dans le vivant, une membrane n'est pas une limite hermétique. Elle sépare deux milieux sans les couper l'un de l'autre, filtre les échanges et adapte son comportement à ce qu'elle rencontre. Elle protège, régule et laisse passer ce qui doit circuler.

Transposé au CIAM, ce principe transforme le statut du couloir. Il devient une épaisseur continue qui isole les salles de musique et absorbe une partie de l'intensité sonore. Les salles fonctionnent alors comme des cellules autonomes, séparées les unes des autres par une zone intermédiaire dans laquelle l'énergie peut progressivement redescendre.

Cette membrane se déforme selon les usages : elle devient cloison, assise, rangement, seuil ou façade. Elle crée ainsi un langage commun à l'ensemble de l'école.



Le couloir habité — vue axiale

LES QUATRE COMPORTEMENTS DE LA MEMBRANE

Séparer

Isoler chaque cellule musicale : aucune salle ne touche sa voisine.

Filtrer

Absorber une part du son et adoucir la transition entre bruit et calme.

Échanger

Laisser la musique se partager là où elle doit l'être — espace jam, salle de concert.

S'adapter

Changer de comportement selon le lieu : cloison, assise, seuil, façade.



Un interstice de la membrane, occupé par les banquettes acoustiques.

LA CIRCULATION — PLAN DU REZ-DE-CHAUSSÉE

Le nouveau plan organise l'école autour d'une circulation continue qui traverse les différentes parties du bâtiment. Elle relie l'entrée, les salles de cours, les anciennes écuries, la salle de concert et la cour intérieure, tout en donnant une lecture plus claire des parcours.


Les salles de musique ne sont plus directement accolées les unes aux autres. Elles deviennent des cellules indépendantes, séparées par l'épaisseur de la membrane. Cette disposition limite les transmissions sonores et ménage des espaces intermédiaires entre les différentes intensités musicales.

Le couloir ne sert donc plus uniquement à distribuer les pièces. Il devient un espace habité, capable d'accueillir l'attente, le repos, les échanges informels et le rangement des instruments.

PLAN PROJET

NIVEAU : RDC

ECHELLE1/100

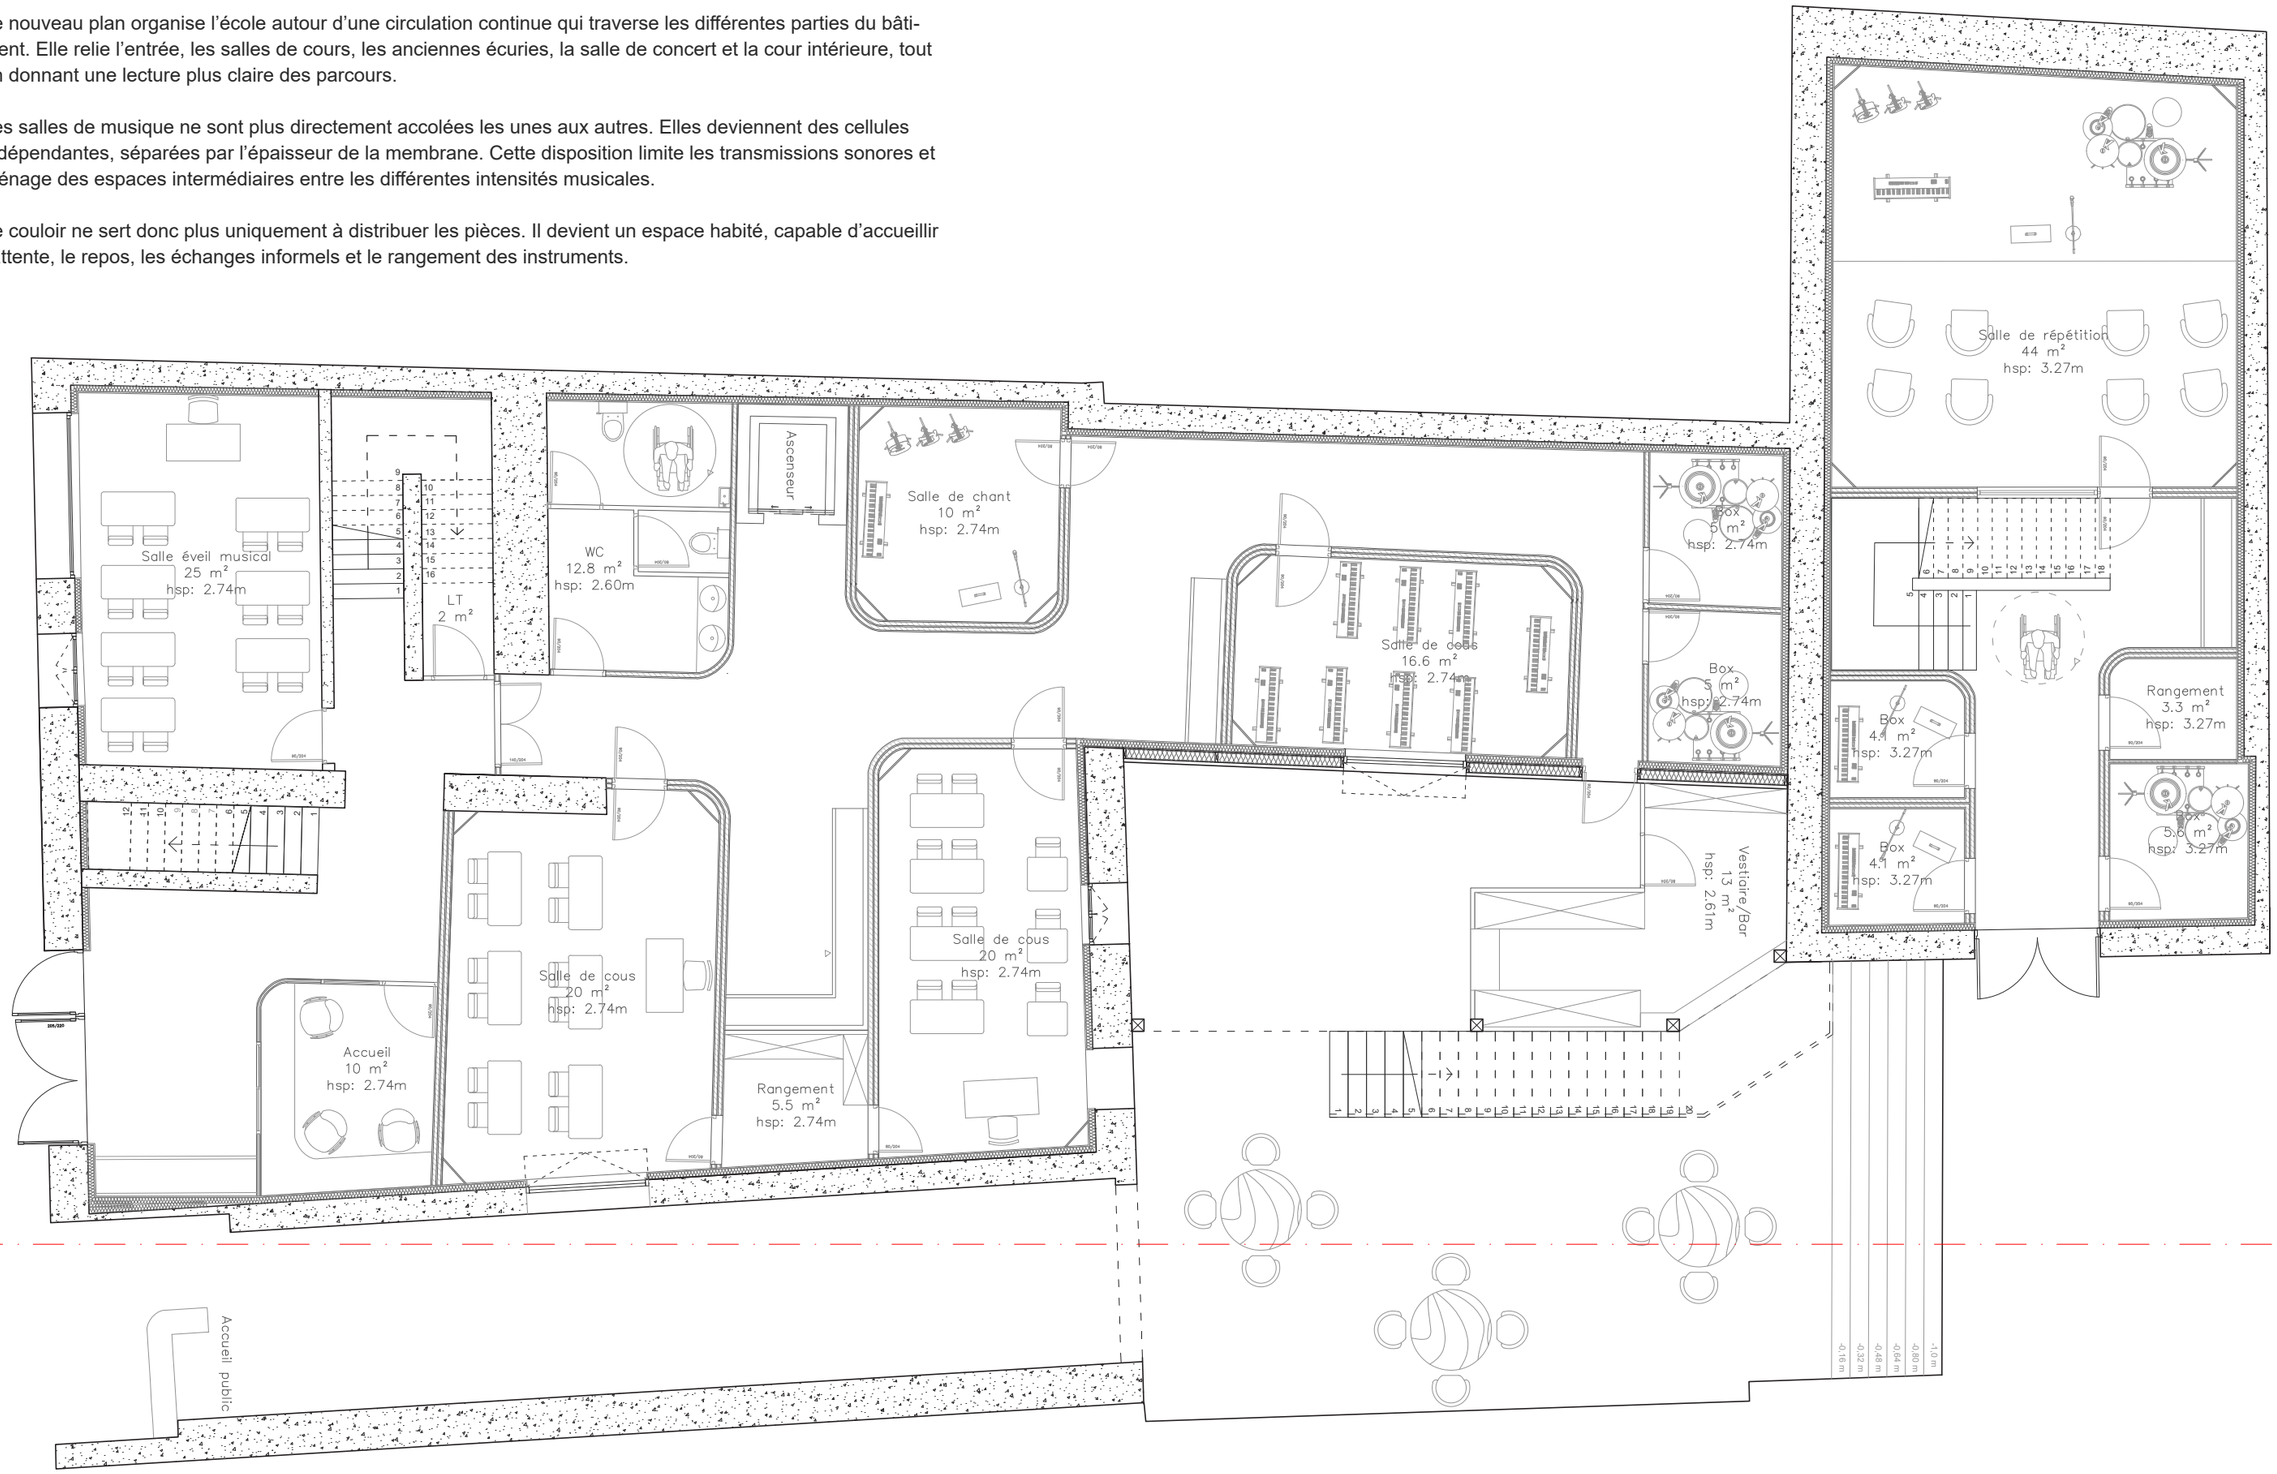


LA CIRCULATION — PLAN DU REZ-DE-CHAUSSÉE

La coupe révèle le projet comme une succession de séquences plutôt que comme une simple distribution verticale. Depuis l'entrée, le visiteur dépose ses affaires, traverse les espaces d'apprentissage, monte vers la salle de concert puis ressort vers la cour et sa terrasse.

À chaque changement de niveau, la membrane accompagne le déplacement et modifie sa forme. Elle resserre certains passages, en élargit d'autres et crée des seuils où l'on peut s'arrêter avant de poursuivre son parcours.

Cette progression permet de relier les différentes architectures présentes sur le site sans effacer leurs particularités. Le bâtiment principal, les anciennes écuries et la cour ne sont plus perçus comme des éléments séparés, mais comme les étapes d'un même cheminement.

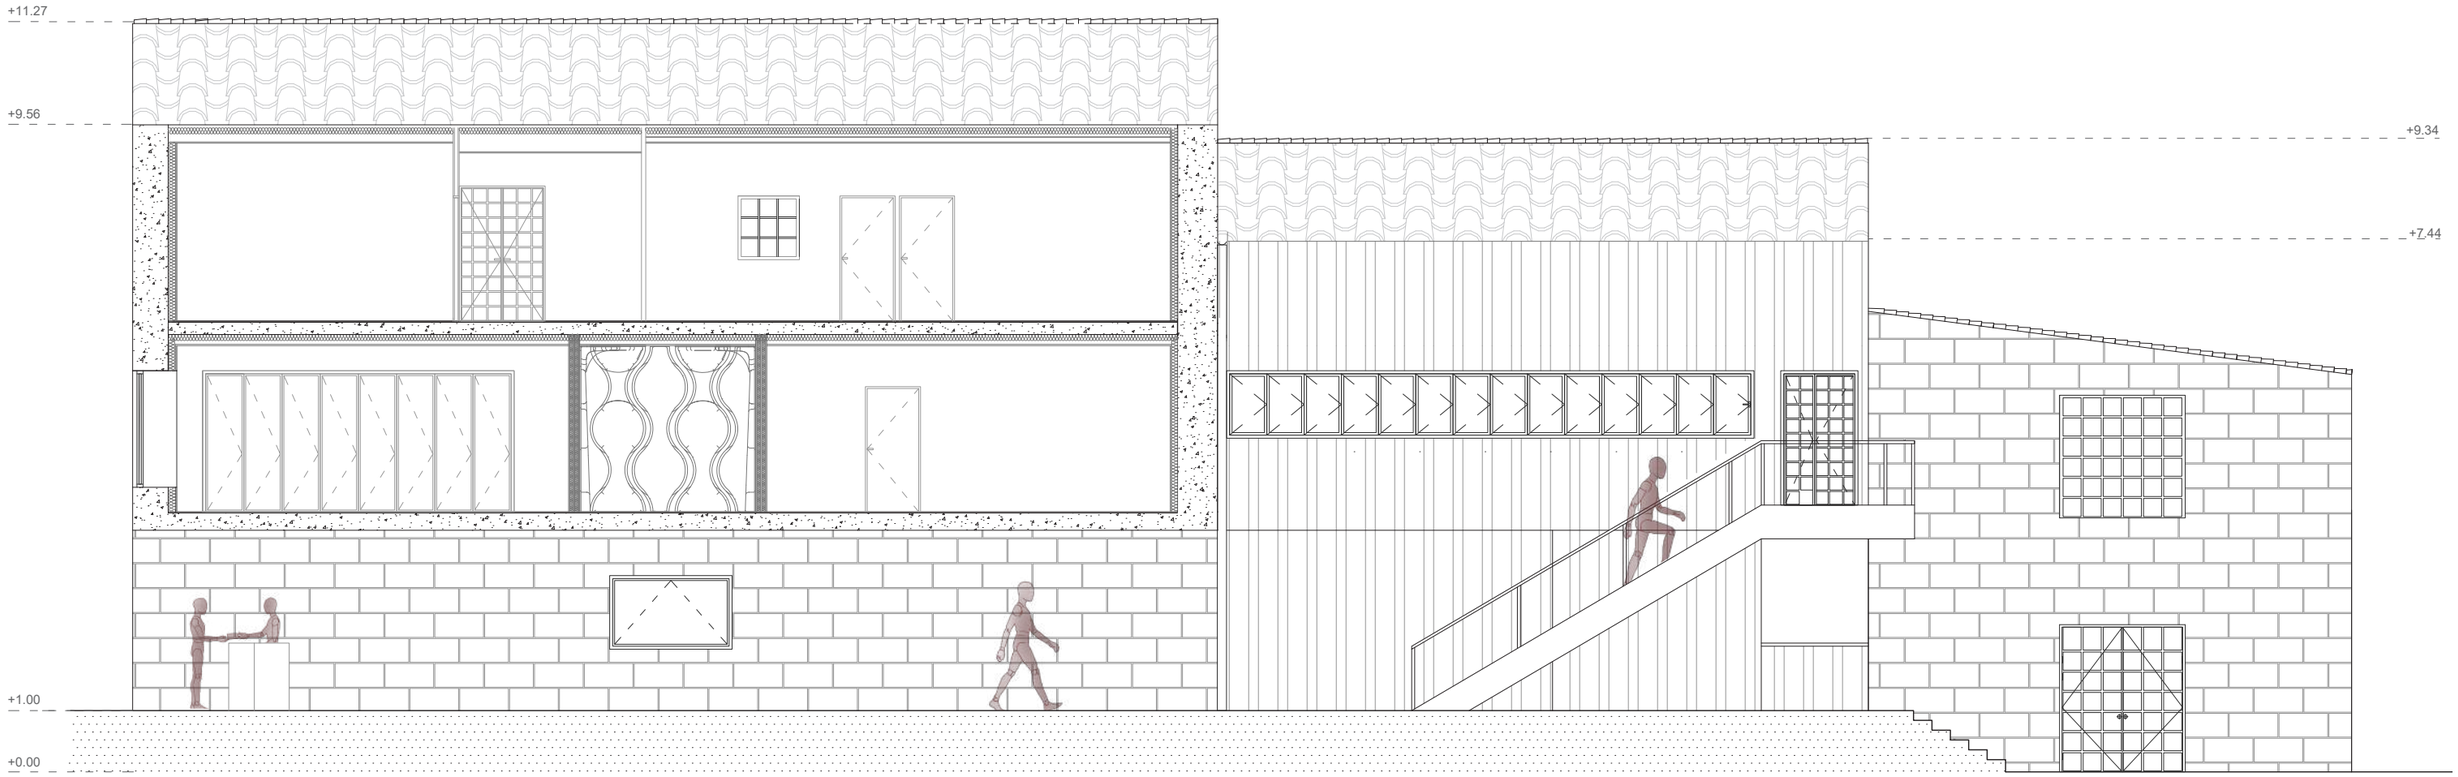

COUPE AA'
ÉCHELLE : 1/100

01

Entres et contrôle

02

Dépose au vestiaire

03

Accès à la salle de concert

04

Entres et contrôle

LE MOBILIER — HABITER LA MEMBRANE

Le mobilier qualifie la circulation : il transforme les interstices du couloir en postures de repos.

Le mobilier prolonge la membrane jusque dans les usages du quotidien. Implantés dans les interstices de la circulation, les dossiers et les banquettes transforment les surfaces du couloir en supports de repos, de rangement et d'échange.

Le système est composé de plusieurs modules combinables, capables de s'adapter à la largeur des passages et aux différentes postures. Il permet de s'asseoir, de s'adosser, de se caler ou de déposer un instrument sans ajouter de mobilier indépendant dans la circulation.

Le garnissage réemploie les anciennes mousses acoustiques du CIAM, destinées à être jetées après les travaux. Associées à une ouate et à un tissu transonore, elles améliorent le confort tout en participant à la réduction de la réverbération sonore.




Assemblage d'angle — dossiers, banquette et module de finition.

SCÉNARIO D'USAGE



01 Je range mon instrument dans les interstices de la banquette.

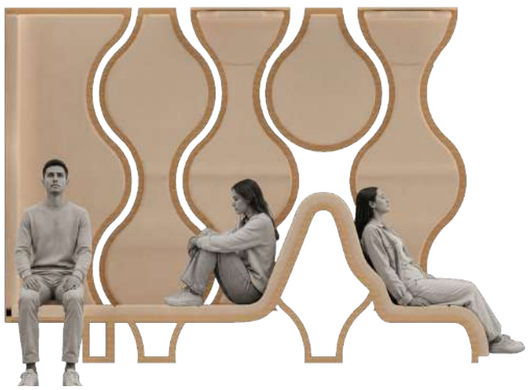

02 Je m'installe dans la position de mon choix, selon mon envie : me reposer, déjeuner ou simplement faire une pause.

PERFORMANCE ACOUSTIQUE — RÉDUCTION DU T20

−26 %	−33 %	−44 %
global	à 500 Hz	à 1000 Hz

Essai comparatif sur prototype à échelle réduite : boîte témoin vide, puis équipée du complexe bois / mousse / tissu.

LE RÈGNE ANIMAL

Long métrage de Thomas Cailley

Le film Le Règne animal imagine une France contemporaine dans laquelle certains humains se transforment progressivement en animaux. Le travail du décor consiste alors à rendre crédible l'apparition de ce phénomène extraordinaire au sein d'environnements volontairement ordinaires et familiers.

Intégré à l'équipe décoration dirigée par Julia Lemaire, j'ai découvert les différentes étapes de fabrication d'un décor de cinéma : lecture du scénario, recherches d'ambiances, préparation des accessoires, interventions sur les décors et présence pendant le tournage.

Cette expérience a modifié ma manière de concevoir l'espace. Contrairement à un intérieur destiné à être habité durablement, un décor est pensé pour être cadré, éclairé et traversé par une caméra. Chaque élément doit servir le récit, révéler un personnage ou accompagner une action.

Contexte	Stage en équipe décoration — long métrage
Année	Été 2022 — stage de première année
Réalisation	Thomas Cailley
Chef décoratrice	Julia Lemaire
Production	Nord-Ouest Films · StudioCanal · France 2 Cinéma · Artémis Productions
Rôle personnel	Stagiaire décoration

Les décors présentés ont été conçus et réalisés par l'équipe décoration sous la direction de Julia Lemaire. Cette page rend compte de ma participation en tant que stagiaire, non d'une création personnelle. Toute image issue du film reste la propriété de la production.



© 2023 Nord-Ouest Films / StudioCanal / France 2 Cinéma / Artémis Productions — photo Ivan Mathie



©BAT 47

MISSION

Conception

Chambre de Nina · organisation de la maison de la fête d'adolescents · définition des ambiances propres à chaque personnage, à partir du scénario · étude du parcours d'un animal dans le décor.

Fabrication et plateau

Montage de décors, dont la tour de la séquence finale · marquage des camions de transport des personnes en mutation · présence au tournage, retouches et réparations en cours de prise.

Objets et graphisme

Accessoires de jeu : copies d'élèves, poème de Nina · signalétique sanitaire du film, affiches distinguant humains et animaux · listing des éléments nécessaires, décor par décor.

NAL

Rénovation d'un appartement locatif

Situé dans le quartier Saint-Michel à Bordeaux, cet appartement ancien devait être entièrement remis à niveau avant sa remise en location. Le projet associe rénovation énergétique, reprise des équipements techniques et réorganisation des usages dans une surface relativement contrainte.

L'intervention conserve autant que possible les réseaux et les qualités existantes du logement afin de maîtriser le coût des travaux. Le parquet ancien est restauré, tandis que la cuisine, la salle d'eau et les rangements sont redessinés pour améliorer le fonctionnement quotidien.

Le projet cherche avant tout à rendre le logement plus clair et plus fluide. Une véritable entrée est créée, la cuisine s'ouvre sur la pièce principale et des verrières permettent à la lumière naturelle d'atteindre les espaces auparavant enclavés.

Contexte	Projet d'agence — L'Atelier D
Année	2025
Programme	Rénovation d'un appartement pour location non meublée
Localisation	Bordeaux — quartier Saint-Michel
Rôle personnel	Conception, pièces graphiques, DCE et suivi de chantier
Focus présenté	Plans, coupe, images de synthèse, essai acoustique
Documents	Photos du projet livré, plans état des lieux et projet

VALEURS AJOUTÉES

01 Entrée clarifiée par un rangement intégré

02 Cuisine ouverte et plus fonctionnelle

03 Verrières pour apporter la lumière naturelle

04 Réemploi du parquet, isolation et remise à neuf



Pièce de vie — la cuisine redessinée structure l'espace sans fermer le volume. ©L'atelier D



Verrière intérieure — apport de lumière dans la chambre et le dégagement ©L'atelier D.



Salle d'eau — réorganisation autour des réseaux existants ©L'atelier D.

RÉORGANISER INTELLIGEMMENT

La transformation repose sur une relecture précise du plan plutôt que sur une restructuration complète de l'appartement. Chaque modification répond à un problème concret : manque de rangement à l'entrée, cuisine trop fermée, pièces secondaires peu éclairées et organisation confuse des sanitaires.

La nouvelle cuisine s'intègre à la pièce de vie et participe pleinement à son aménagement. Une cloison de rangement marque le seuil de l'appartement, tandis que la salle d'eau est rapprochée des arrivées et des évacuations existantes pour limiter les interventions techniques.

Les verrières deviennent enfin des outils de distribution de la lumière. Elles permettent de préserver l'intimité des pièces tout en créant des relations visuelles et lumineuses entre la chambre, le dégagement et les espaces de vie.




Pièce de vie - ©L'atelier D.



Couloir - ©L'atelier D.


PLAN EDL

NIVEAU : R+4
ECHELLE1/100

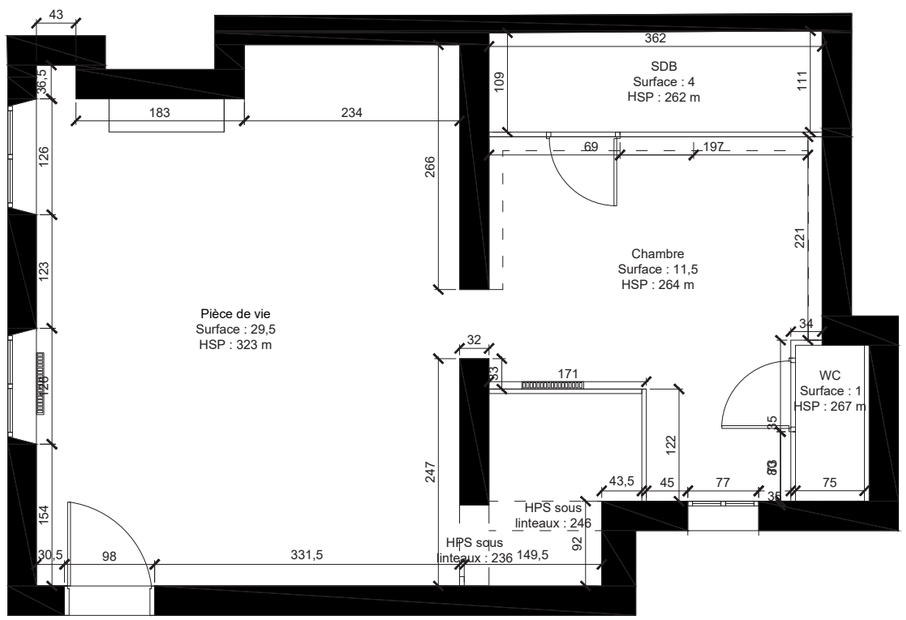

PLAN PROJET

NIVEAU : R+4
ECHELLE1/100

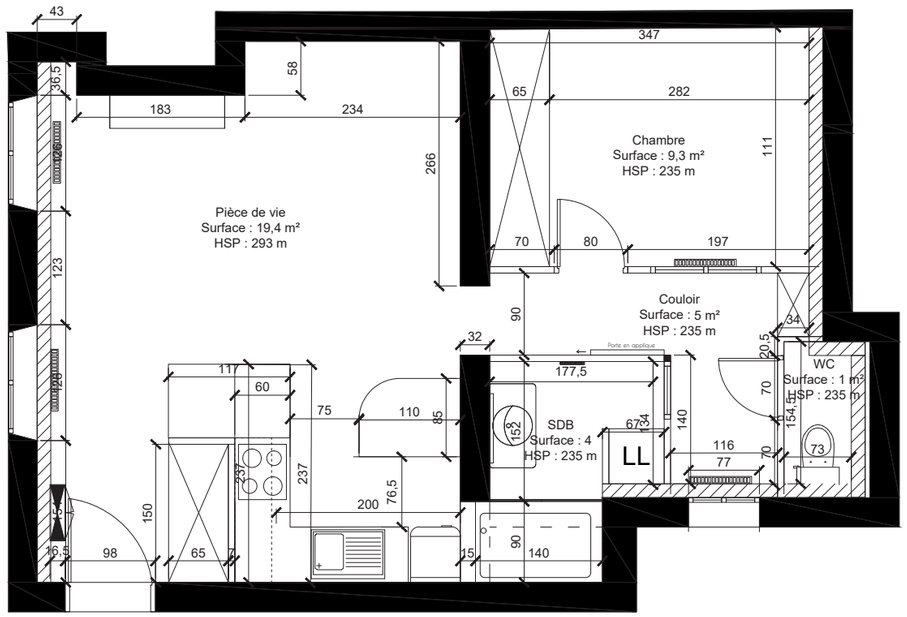

LECTURE DU PROJET

01 *Créer un seuil*

Une cloison de rangement délimite l'entrée et complète la cuisine.

02 *Optimiser les réseaux*

La salle d'eau s'organise au plus près des arrivées et évacuations existantes.

03 *Apporter la lumière*

Des verrières désenclavent la chambre et amènent la lumière au dégagement.

04 *Valoriser l'existant*

Le parquet existant est conservé, poncé et vitrifié pour préserver le cachet du lieu.

OBADIA

Adaptation d'un appartement en Airbnb premium

Cet appartement situé à proximité d'un golf devait être transformé en location saisonnière premium, sans modifier lourdement son organisation existante. Le projet s'appuie donc principalement sur les ambiances, la couleur et le mobilier pour donner au logement une identité immédiatement reconnaissable.

Le vert olive et le bordeaux construisent un univers profond et chaleureux, inspiré des codes du golf et de l'hôtellerie haut de gamme. Les plafonds peints prolongent les couleurs des murs et deviennent une véritable cinquième façade, capable de différencier les pièces et de renforcer leurs proportions.

Chaque intervention est pensée pour enrichir l'expérience du séjour : cuisine complétée, couchages optimisés, rangements intégrés et mobilier sur mesure structurant la pièce principale.

Contexte	Projet d'agence — L'Atelier D
Année	2026
Programme	Location saisonnière premium · 4 couchages
Localisation	Villenave-D'ornon — proximité du golf
Rôle personnel	Conception d'ambiance, aménagement, visuels et pièces graphiques
Focus présenté	Couleur, atmosphère et mobilier structurant
Documents	Visuels du dossier APD


VALEURS AJOUTÉES

01 Requalification par l'atmosphère


02 Plafonds peints comme cinquième façade

03 Meuble-filtre entre espace repas et séjour

04 Cuisine et couchages adaptés à l'usage Airbnb

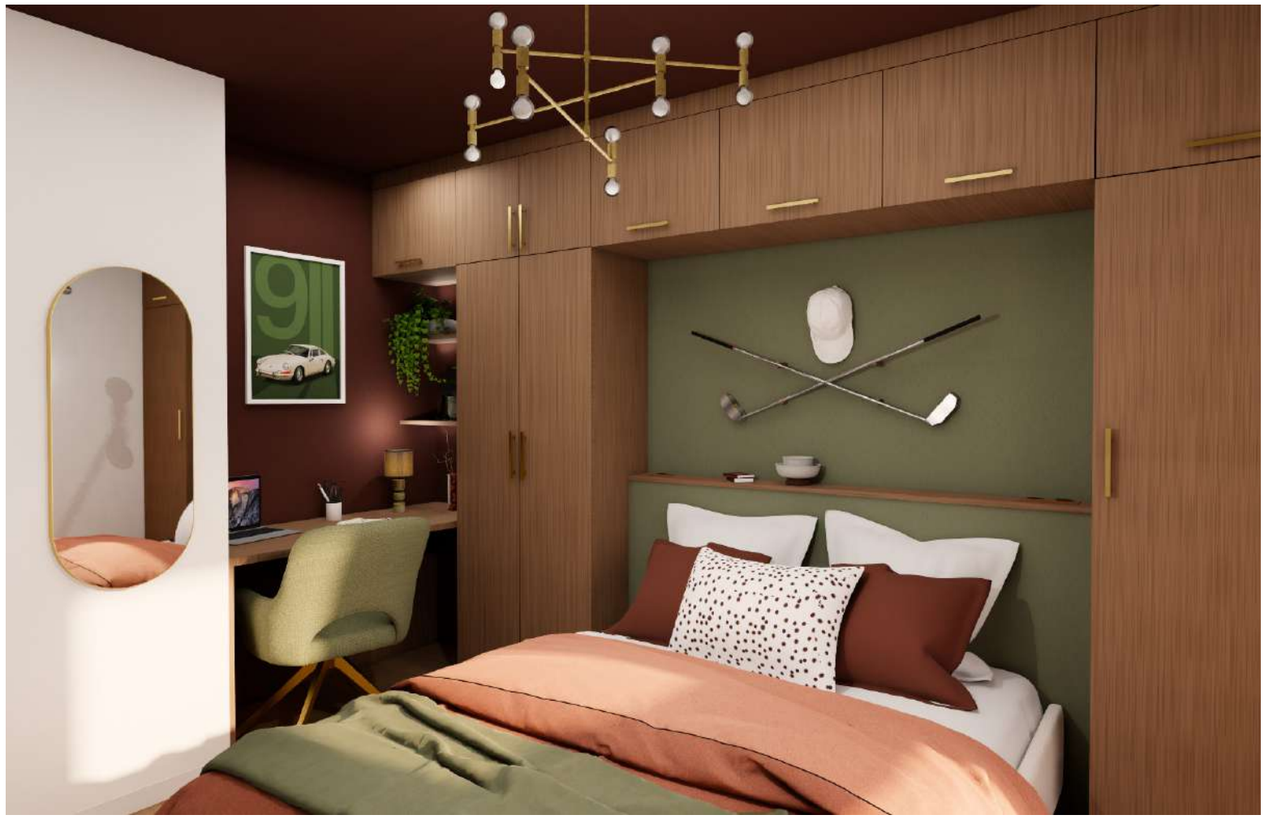

Chambre — alcôve, rangements et plafond coloré composent un cocon.

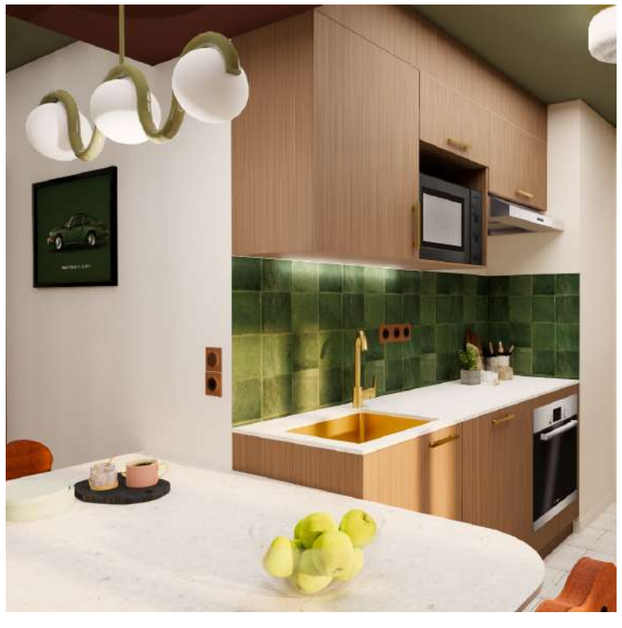

Cuisine refaite a neuf en conservant le sol et les emplacements



Séjour — palette olive / bordeaux et références au golf installent le positionnement.

DONNER UNE IDENTITÉ SANS RESTRUCTURER LE PLAN

Une membrane habitée : le couloir cesse d'être un passage pour devenir l'organe qui sépare, filtre et régule les intensités de l'école.

Le projet montre qu'un changement d'atmosphère peut profondément transformer la perception d'un appartement sans modifier son plan. Les couleurs sombres, les matières chaleureuses et les détails en laiton font basculer un intérieur relativement neutre vers une adresse locative plus singulière et plus qualitative.

Dans la pièce principale, un meuble-filtre en bois organise les usages sans fermer le volume. Côté séjour, il accueille la télévision et les rangements. Côté repas, il se prolonge en banquette et accompagne la table, créant une limite fonctionnelle mais visuellement perméable.

La cuisine et le mobilier convertible répondent enfin aux contraintes de la location saisonnière. L'appartement peut accueillir quatre personnes tout en conservant une lecture claire et une circulation confortable.



Espace repas — table intégrée et banquette dans l'épaisseur du claustra.



Esapce repas



Espace bureau de la chambre.

LECTURE DU PROJET

01 *Travailler la cinquième façade*

Les plafonds colorés prolongent l'ambiance, renforcent l'identité de chaque pièce et donnent une profondeur immédiate aux volumes.

02 *Filtrer les usages*

Le claustra organise la pièce de vie, concentre télévision, rangements et banquette, tout en maintenant la continuité visuelle.

03 *Installer un univers*

Palette profonde, bois chaleureux, détails laiton et références au golf construisent une image identifiable et premium.

04 *Optimiser l'usage locatif*

Canapé convertible, table intégrée et cuisine complète répondent à quatre couchages sans surcharger l'espace.

HEGOBURU

Réhabilitation d'une échoppe familiale

Le projet concerne la réhabilitation d'une échoppe familiale et d'un ancien garage, initialement séparés par un jardin. L'enjeu est de réunir ces deux constructions sans faire disparaître l'espace extérieur qui leur apporte lumière, recul et intimité.

Une extension mesurée transforme une partie du jardin en salle à manger traversante. Placé entre l'échoppe et l'ancien garage, ce nouvel espace devient à la fois un lieu de repas, un passage quotidien et une articulation entre les différentes parties de la maison.

Le patio conservé reste visible depuis les principales pièces de vie. Il introduit une respiration au centre du plan et permet à la lumière naturelle d'accompagner la circulation jusqu'à la chambre parentale située au fond de la parcelle.

Contexte	Projet d'agence — L'Atelier D
Année	2025
Programme	Rénovation d'une échoppe avec extension
Localisation	Bègles
Rôle personnel	Conception, plans, visuels
Focus présenté	Patio habité et circulation
Documents	Plan et visuel 3D de l'APD

VALEURS AJOUTÉES


01 Patio habité comme espace de liaison

02 Extension mesurée pour reconnecter les volumes


03 Extérieur conservé comme apport de lumière



Salle à manger — le patio habité devient à la fois lieu de repas et espace de transition.

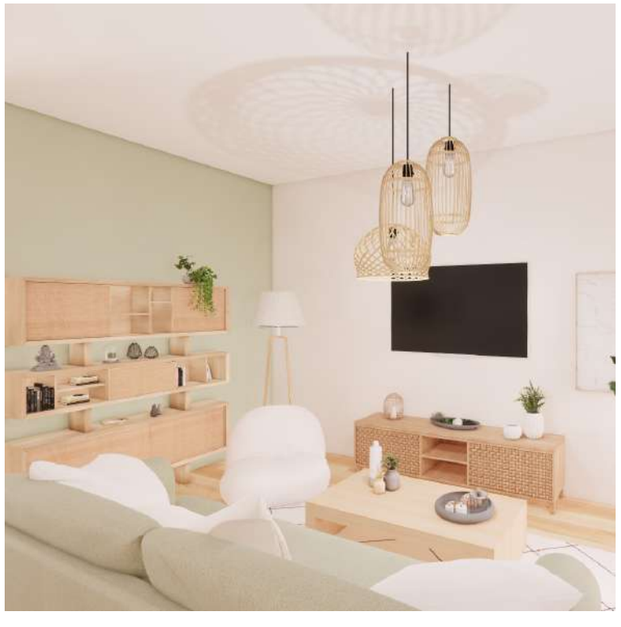

Pièce de vie — une atmosphère douce et lumineuse ouverte sur le patio.

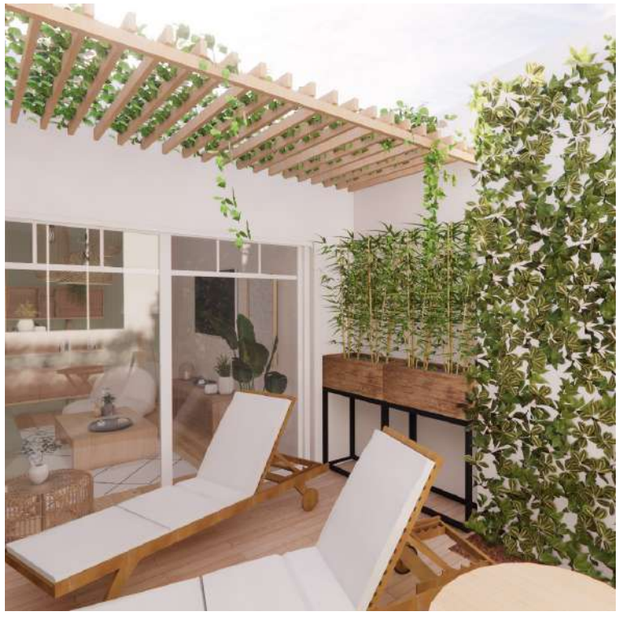

Terrasse — un extérieur conservé qui prolonge les usages quotidiens.

HABITER LA CIRCULATION PAR LE PATIO

La transformation repose sur une relecture précise du plan plutôt que sur une restructuration complète de l'appartement. Chaque modification répond à un problème concret : manque de rangement à l'entrée, cuisine trop fermée, pièces secondaires peu éclairées et organisation confuse des sanitaires.

La nouvelle cuisine s'intègre à la pièce de vie et participe pleinement à son aménagement. Une cloison de rangement marque le seuil de l'appartement, tandis que la salle d'eau est rapprochée des arrivées et des évacuations existantes pour limiter les interventions techniques.

Les verrières deviennent enfin des outils de distribution de la lumière. Elles permettent de préserver l'intimité des pièces tout en créant des relations visuelles et lumineuses entre la chambre, le dégagement et les espaces de vie.




Espace repas



Cuisine


PLAN EDL

NIVEAU : RDC
ECHELLE1/100

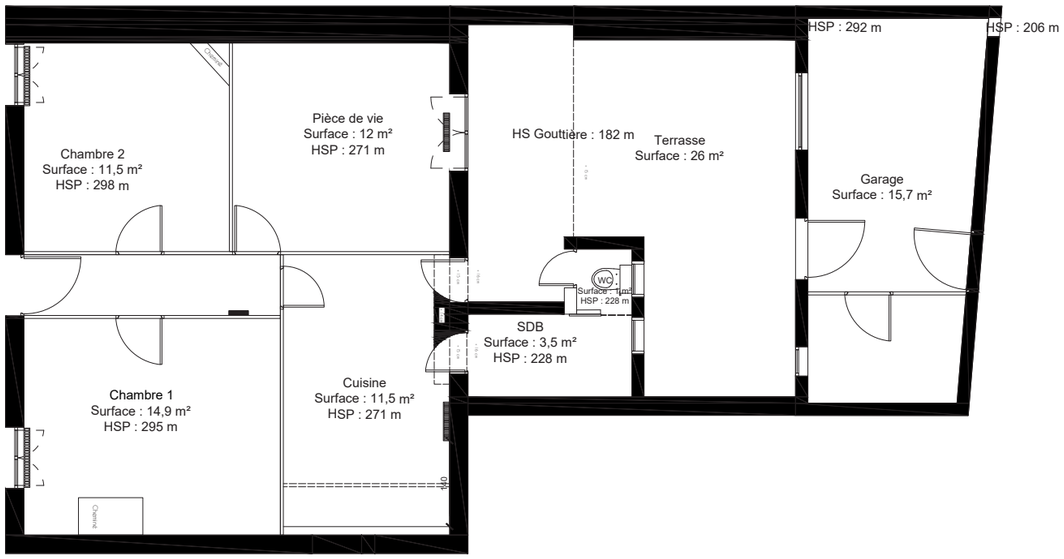

PLAN PROJET

NIVEAU : RDC
ECHELLE1/100

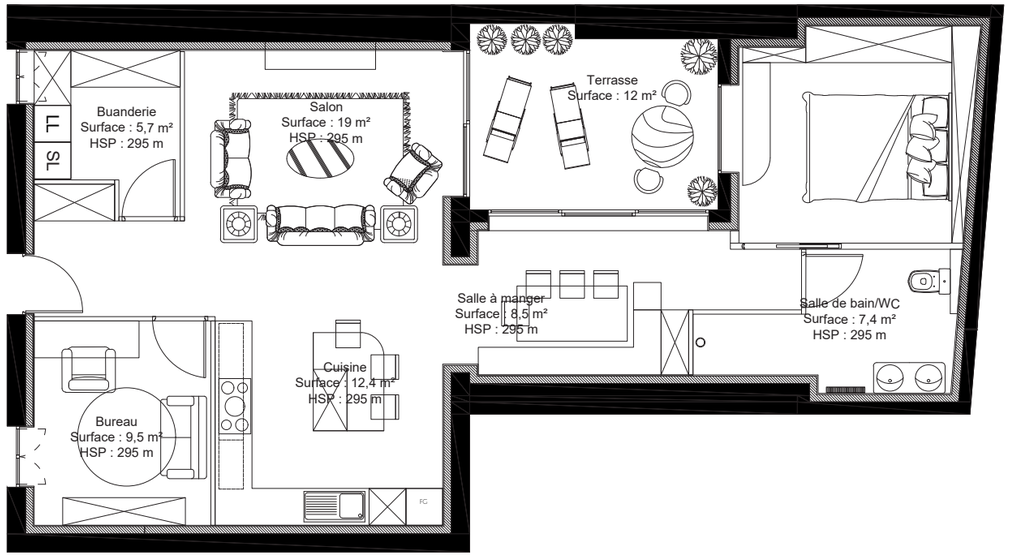

LECTURE DU PROJET

01 *Reconnecter les volumes*

L'extension et le patio relient l'échoppe existante à l'ancien garage pour former un ensemble habitable continu.

02 *Habiter le passage*

La circulation devient une salle à manger traversante avec banquette, au cœur des usages quotidiens.

03 *Organiser autour du vide*

Pièce de vie, cuisine et chambre s'ouvrent autour de l'extérieur conservé, source de lumière et de respiration.

04 *Isoler l'espace nuit*

La chambre parentale est placée au fond de la parcelle, au calme, avec un rapport direct à la terrasse.

DUBON

Rénovation d'un appartement de 180 m²

Destiné à un couple de retraités, le projet porte sur la rénovation d'un appartement de 180 m² situé à Caudéran. La transformation du plan reste volontairement mesurée : l'essentiel de l'intervention repose sur la création de plusieurs meubles sur mesure adaptés aux habitudes et aux objets des clients.

Le mobilier devient un outil d'architecture intérieure. Il permet de ranger, de dissimuler les éléments techniques, de séparer les usages et de donner une identité cohérente aux différentes pièces, sans multiplier les cloisons.

Trois dispositifs structurent particulièrement le projet : le meuble d'entrée dissimulant l'accès à la cuisine, la bibliothèque d'angle intégrant la télévision et la platine vinyle, puis le séparateur entre la salle à manger et le bureau, conçu comme un filtre lumineux.

Contexte	Projet d'agence — L'Atelier D
Année	2025-2026
Programme	Appartement privé · rénovation et mobilier sur mesure
Localisation	Caudéran
Rôle personnel	Conception, aménagement, mobilier sur mesure et visuels, DCE
Focus présenté	Mobilier structurant et dispositifs de séparation
Documents	Visuel APD et dossier de consultation sur mesure

VALEURS AJOUTÉES

01 Le mobilier sur mesure comme structure du projet

02 Séparer les usages sans perdre la lumière

03 Intégrer rangement, identité et confort dans chaque pièce



Séparation repas / bureau — un meuble-filtre mêlant transparence, bibliothèque et rangement bas.



Entrée — un ensemble symétrique dissimule l'accès à la cuisine et recompose le seuil.



Séjour — la bibliothèque d'angle réunit niche TV, platine vinyle et stockage des livres.

TRAVAILLER L’ESPACE PAR LE MOBILIER

Dans l’entrée, le mobilier est pensé comme une façade intérieure continue. Sa composition symétrique donne l’apparence d’un grand vestiaire, alors que certaines portes dissimulent en réalité l’accès à la cuisine. Penderies, chaussures et équipements techniques disparaissent dans un ensemble calme et décoratif.

Dans le séjour, la bibliothèque habite l’angle de la pièce. Elle rassemble les livres, la télévision, la platine vinyle, les appareils techniques et plusieurs niches d’exposition, tout en dessinant une séquence plus enveloppante autour du salon.

Entre le bureau et la salle à manger, le troisième meuble marque une limite sans interrompre la lumière. Son soubassement accueille les rangements, tandis que sa partie haute combine étagères et panneaux vitrés décoratifs.



Bureau



Cuisine

MEUBLE D’ENTRÉE



Ce meuble est pensé comme une façade continue entre entrée et cuisine. Sa composition symétrique donne l’impression d’un grand vestiaire, alors que certaines portes ouvrent en réalité vers la cuisine. Il intègre penderies, tiroirs à chaussures, niches et tableau électrique, pour faire disparaître les fonctions techniques dans un ensemble calme et décoratif.

MEUBLE TV



La bibliothèque d’angle répond à plusieurs usages en un seul volume : ranger les livres, intégrer la télévision, accueillir la platine vinyle, dissimuler les équipements et ménager des niches d’exposition. Sa forme enveloppante transforme un angle du séjour en véritable pièce de mobilier, à la fois fonctionnelle et identitaire.

SÉPARATEUR REPAS / BUREAU



Le séparateur répond à la demande de distinguer salle à manger et bureau sans perdre la lumière. La partie basse devient vaisselier et rangement, tandis que la partie haute associe étagères, objets exposés et panneaux vitrés décoratifs. Le meuble agit comme un filtre : il marque une limite tout en conservant les perspectives entre les deux pièces.

MONGIRON

Rénovation d'une bâtisse en pierre — loft et caveau de dégustation

Réalisé pour des clients australiens, le projet concerne la rénovation partielle d'une grande bâtisse en pierre située dans le secteur de Saint-Émilion. Le travail est mené en anglais et en collaboration avec un maître d'œuvre chargé du suivi architectural et des modifications de façade.

L'intervention cherche à préserver le caractère minéral et historique du lieu tout en proposant une interprétation contemporaine de la demeure française. La pierre existante, les boiseries, les tissus et la serrurerie sombre composent un vocabulaire commun aux différents espaces.

Le projet se concentre principalement sur le sous-sol, transformé en deux séquences complémentaires : un loft destiné à la réception et un caveau consacré à la conservation, à la présentation et à la dégustation du vin.

Contexte	Projet d'agence — L'Atelier D
Année	2025-2026
Programme	Rénovation partielle d'une bâtisse en pierre
Localisation	Montgiron, secteur Saint-Émilion
Rôle personnel	Conception, ambiance, aménagement et visuels
Focus présenté	Loft de réception et caveau de dégustation
Documents	APD loft, APD caveau et visuels 3D

VALEURS AJOUTÉES

01 Réinterpréter le château à la française en sous-sol

02 Mettre en valeur la pierre, le bois et les matières nobles

03 Articuler réception, dégustation et conservation



Loft — un volume de réception inspiré de la demeure classique, entre pierre, bois et lumière.



Caveau — une pièce de dégustation structurée par le mobilier et les matières sombres.



Salon / bibliothèque — une écriture chaleureuse qui prolonge l'esprit de la bâtisse.

HABITER LE SOUS-SOL
COMME UN LOFT DE RÉCEPTION

Dans le loft, l’intervention cherche moins la démonstration que la justesse d’ambiance. Volumes généreux, pierre apparente, charpente claire et serrurerie noire composent un univers inspiré des demeures anciennes, sans tomber dans la reconstitution décorative.

Les séquences de salon, bibliothèque et salle à manger s’organisent comme un espace de réception habité, à la fois chaleureux et lumineux. Les changements de niveau, la relation au paysage et le mobilier aux lignes classiques renforcent la qualité domestique de cet ensemble.



Salle à manger — une séquence plus verticale, structurée par l’escalier et la grande table.



Vue complémentaire — l’ambiance du loft articule matière minérale, bois et lumière.



Bibliothèque / salon — un registre domestique et feutré, entre réception et lecture.

CONCEVOIR UN CAVEAU COMME ESPACE DE DÉGUSTATION

Le caveau prolonge l'univers du loft par une écriture plus enveloppante. Le plafond bois, les boiseries foncées, les appliques et les éléments inspirés des tonneaux installent une ambiance de dégustation directement liée au monde viticole.

Les rangements périphériques, la table centrale de présentation et la réserve attenante composent un ensemble lisible, pensé autant pour la conservation que pour la réception. L'espace assume un caractère plus scénographié, entre cave de collection et salon de dégustation.



Caveau principal — une pièce de dégustation structurée par le mobilier périphérique et l'îlot central.



WC



Salon de dégustation — une séquence plus informelle, propice à l'attente et à la conversation.

OSE

LA MAISON RESSOURCE - CENTRE D'ACCUEIL POUR LES ENFANTS EN DIFFICULTÉS

La Maison Ressource accueille des enfants et des adolescents confrontés à des situations personnelles difficiles. Le projet cherche à effacer l'image institutionnelle du centre pour retrouver les repères familiers, rassurants et quotidiens d'une maison.

Les matières boisées, les couleurs poudrées et les formes arrondies composent un environnement doux, sans devenir fragile. Chaque aménagement doit résister à un usage collectif intensif, être facilement entretenu et répondre aux contraintes de sécurité propres à l'établissement.

L'architecture intérieure participe ainsi directement à l'accompagnement des jeunes. Elle ne se limite pas à décorer les espaces, mais cherche à rassurer, contenir et offrir des possibilités de retrait dans un cadre lisible et protecteur.

Contexte	Projet d'agence — L'Atelier D
Année	2025-2026
Programme	Centre d'accueil pour enfants et adolescents en difficultés
Localisation	Paris
Rôle personnel	Concept, ambiances, mobilier et matériaux ERP et sécurisant
Focus présenté	Chambres, espaces communs et sécurité d'usage
Documents	Dossier concept, APS et visuels 3D

VALEURS AJOUTÉES

01 Transformer un centre d'accueil en véritable lieu de vie

02 Créer des chambres cocons, individuelles ou partagées

03 Concilier douceur, sécurité et résistance des aménagements


04 Faire en sorte que les enfants se sentent comme à la maison



Chambre collective — des zones de retrait enveloppantes dans un espace partagé.



Espace repas — une ambiance domestique, douce et lisible pour le quotidien.

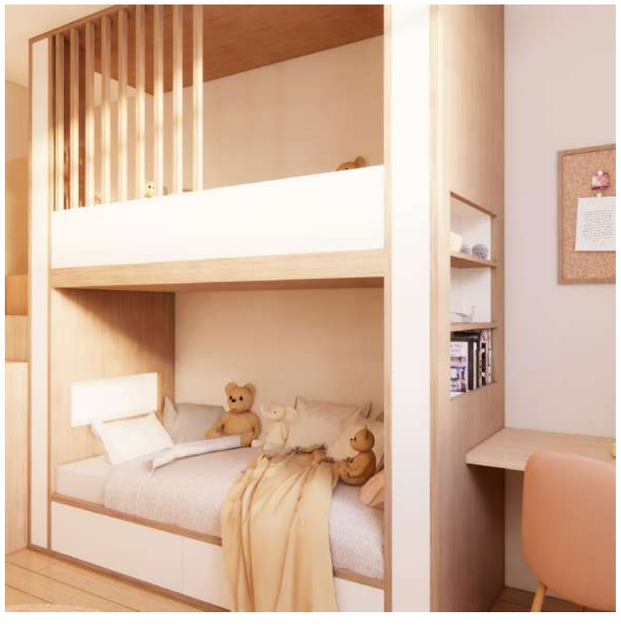


Chambre — un mobilier intégré qui structure le couchage, le travail et le rangement.

CHAMBRES ET ESPACES COMMUNS

Dans les chambres, le mobilier sur mesure regroupe le couchage, le bureau, les rangements et les espaces de retrait. Les lits prennent la forme de niches enveloppantes qui donnent à chaque enfant un territoire identifiable, y compris dans les chambres partagées.

Les espaces communs prolongent cette approche avec des formes simples, des matières chaleureuses et des couleurs capables de différencier les usages. L'objectif est de recréer une ambiance domestique dans laquelle il est possible de manger, discuter, travailler ou se reposer sans ressentir constamment le cadre de l'institution.

Les protections murales, les matériaux lavables et l'éclairage nocturne bas assurent enfin la sécurité des déplacements tout en évitant une ambiance trop technique ou hospitalière.

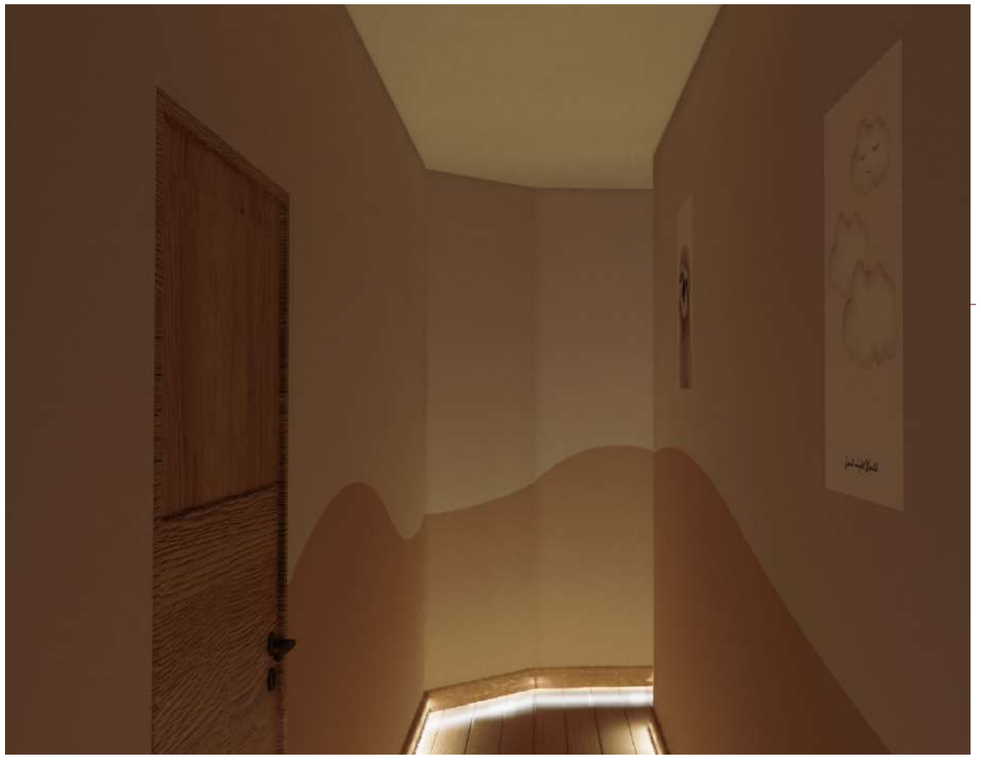

Couloir — un guidage nocturne doux accompagne les déplacements.



Espace commun — des formes arrondies et une palette chaleureuse pour rompre avec l'image institutionnelle.

LECTURE DU PROJET

01 *Rassurer*

Des teintes douces, du bois et des formes courbes pour créer des repères familiers.

02 *Contenir*

Les couchages intégrés dessinent des espaces refuge à l'intérieur des chambres.

03 *Résister*

Matériaux lavables, protections murales et mobilier solidaire sécurisent les usages.

04 *Guider*

La lumière basse facilite les circulations nocturnes sans éclairage agressif.

LE REFUGE

Imaginer une salle de pause comme un refuge hors du temps

Le projet consiste à réaménager la salle de pause des salariés de CDC Habitat à Bruges. Réalisé dans le cadre d'un partenariat avec l'entreprise, il a été sélectionné comme projet lauréat parmi les différentes propositions présentées par l'école.

Pensé dans un contexte post-Covid, le lieu doit offrir une véritable déconnexion avec l'environnement de travail. Le projet s'inspire des refuges rencontrés au cours d'une randonnée : des lieux isolés dans lesquels on peut manger, échanger, se reposer et reprendre son souffle avant de repartir.

La salle se divise ainsi en deux atmosphères complémentaires : une clairière lumineuse ouverte vers l'extérieur et un espace plus sombre, inspiré des refuges de montagne et des hôtels capsules.


Contexte	Projet d'école — partenariat CDC Habitat
Année	2023
Programme	Salle de pause et espaces de repos
Localisation	Bruges, près de Bordeaux
Rôle personnel	Concept, aménagement, ambiances, dossier technique
Focus présenté	Projet lauréat
Documents	Plan texturé, visuels 3D

VALEURS AJOUTÉES


01 Parcours immersif inspiré du refuge et de la clairière

02 Continuité intérieur / extérieur grâce aux vitrages accordéon


03 Double ambiance : restauration conviviale et zone de repos

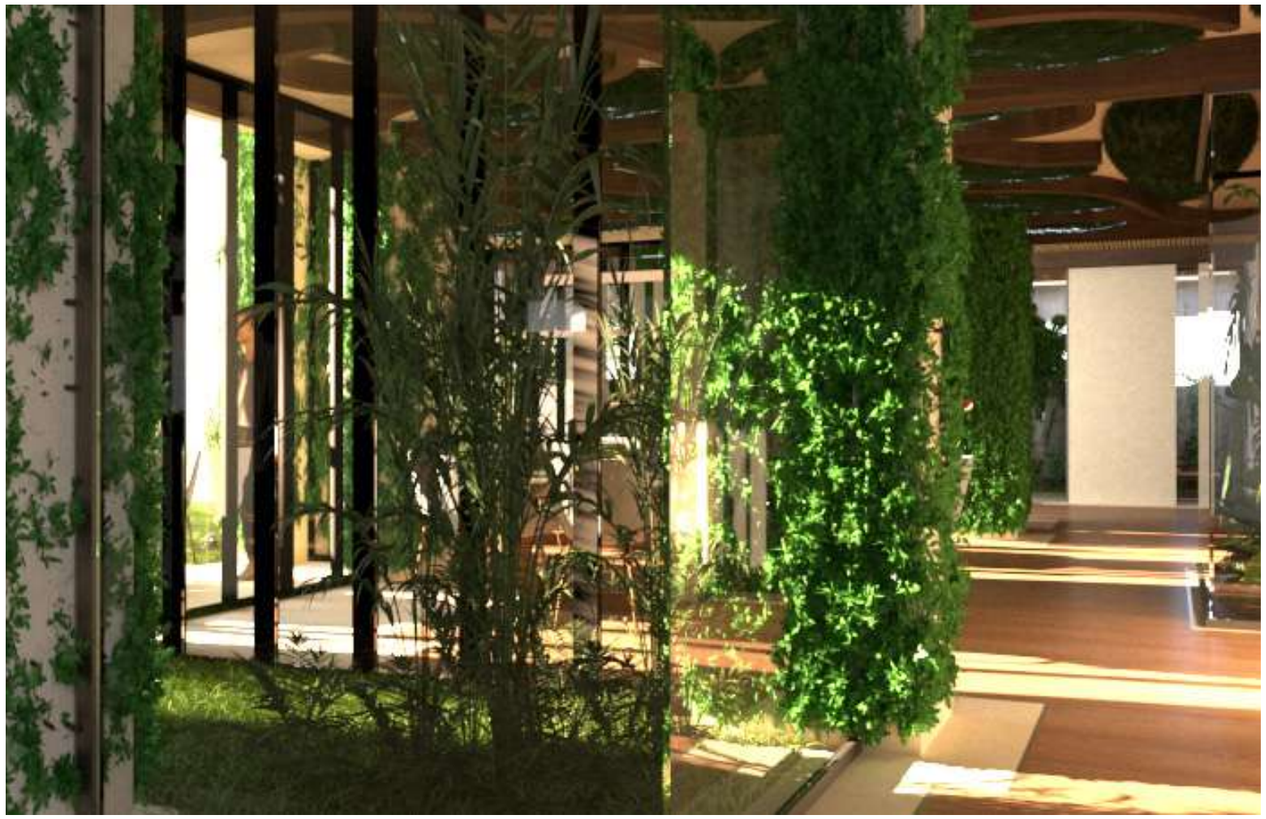

Couloir menant à la cuisine, donnant l'impression d'apercevoir une clairière à travers les « arbres ».

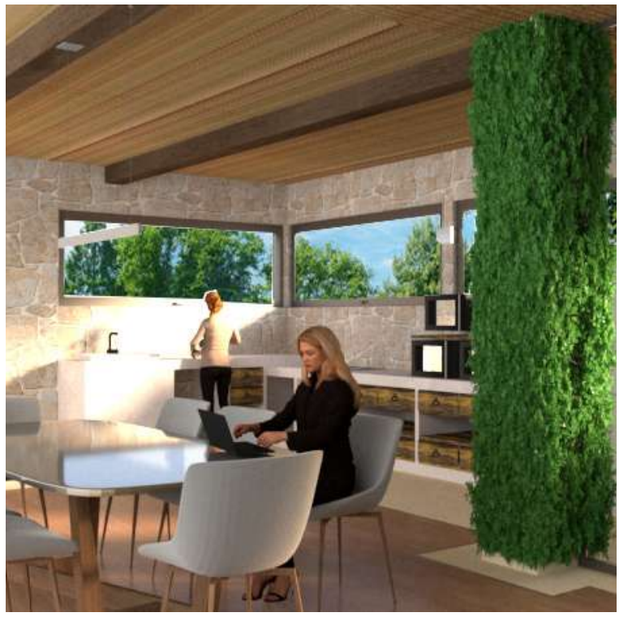

Cuisine, espace repas (la clairière)

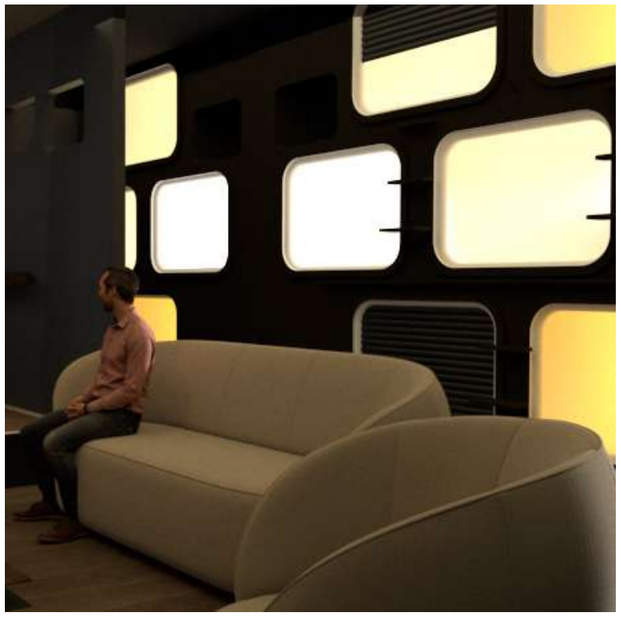

Espace de repos type hôtel capsule pour faire une pose

CHAMBRES ET ESPACES COMMUNS

Après la séquence lumineuse de la cuisine et de la salle à manger, le projet propose un second espace volontairement plus sombre et plus silencieux. Cette rupture permet de choisir entre une pause collective et un moment de retrait individuel.

L'ambiance s'inspire des refuges de montagne et des hôtels capsules. Les tons foncés, les volumes enveloppants, la moquette et les assises profondes créent un environnement dans lequel les salariés peuvent s'isoler, lire, écouter de la musique ou simplement fermer les yeux.

La salle de pause devient ainsi un lieu complet, capable de répondre à différents besoins au cours de la journée. Elle ne propose pas une seule manière de se reposer, mais plusieurs degrés de convivialité, de calme et de déconnexion.




Couloir — un guidage nocturne doux accompagne les déplacements.



Couloir — un guidage nocturne doux accompagne les déplacements.

PLAN TEXTURÉ

NIVEAU : RDC
ECHELLE1/100

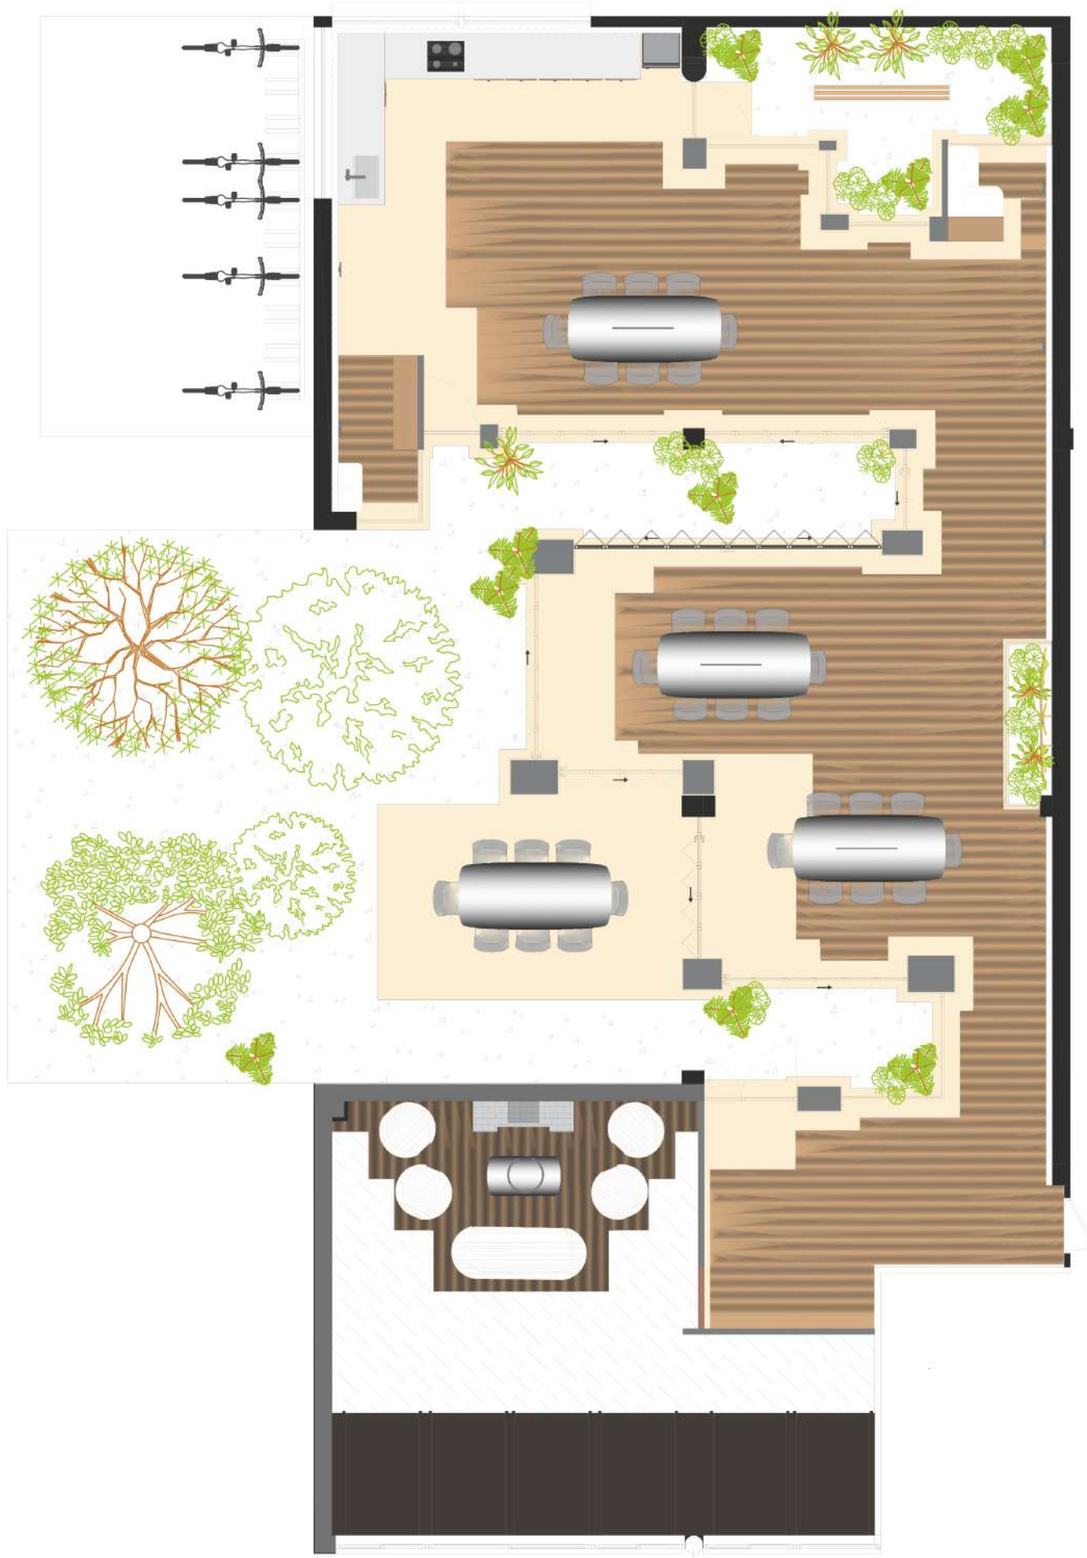

FRACTURE

Canapé-salon convertible et modulable

Fracture est composé de huit éléments indépendants : sept assises en portion de cercle, dont trois équipées d'un dossier, et un module central réversible. Leur combinaison permet de passer d'un salon circulaire à plusieurs configurations plus libres.

Lorsque les éléments sont séparés, chacun devient un fauteuil, une banquette ou une assise d'appoint. Le salon peut alors s'adapter au nombre de personnes, à la taille de la pièce ou au type d'échange recherché.

Une fois réunis, les modules reconstituent une forme circulaire continue. Le centre complète la surface et permet au canapé de devenir un couchage, sans faire appel au mécanisme traditionnel d'un canapé-lit.

Contexte	Concours design — « Quel canapé demain ? »
Année	2023–2024
Programme	Canapé-lit adapté aux nouveaux modes de vie
Organisateur	La Maison Convertible
Rôle personnel	Concept, design produit, modélisation et rendu
Focus présenté	Conversation circulaire, modularité et couchage
Documents	Visuels 3D, dispositions, matériaux et géométraux

VALEURS AJOUTÉES

01 Faire du canapé un salon complet

02 Replacer les usagers face à face

03 Réunir modularité, convivialité et couchage



Vue produit — une géométrie circulaire pensée comme un salon complet.



Mise en situation — forme lit.



Mise en situation — une assise qui favorise la discussion.

DÉCOMPOSER POUR RECOMPOSER LE SALON

Le dessin du mobilier repose sur le contraste entre un socle en bois sombre et des assises textiles plus claires. La base accompagne la forme circulaire du canapé et crée une continuité visuelle entre les différents éléments, même lorsqu'ils sont séparés.

Ses ondulations intègrent de petits espaces de rangement et participent à l'identité organique du projet. Les dossiers reprennent la courbe générale tout en conservant une hauteur suffisamment contenue pour ne pas isoler les occupants les uns des autres.

Les modules sont conçus pour pouvoir être déplacés, retournés et assemblés simplement. L'élément central peut ainsi compléter le couchage, devenir une assise supplémentaire ou se retourner pour former une table basse.



Les éléments structurels sont réalisés en noyer brun. Leur forme ondulée allège le socle tout en créant de petits espaces de rangement intégrés, notamment pour les livres.

Les coussins sont habillés d'un tissu d'ameublement LEGACY Velours, choisi pour son toucher doux, sa résistance et sa teinte claire contrastant avec le bois.

Des aimants intégrés à la structure permettent d'assembler facilement les différents modules, tout en facilitant leur séparation et leur reconfiguration.

EXEMPLES DE DISPOSITIONS







